


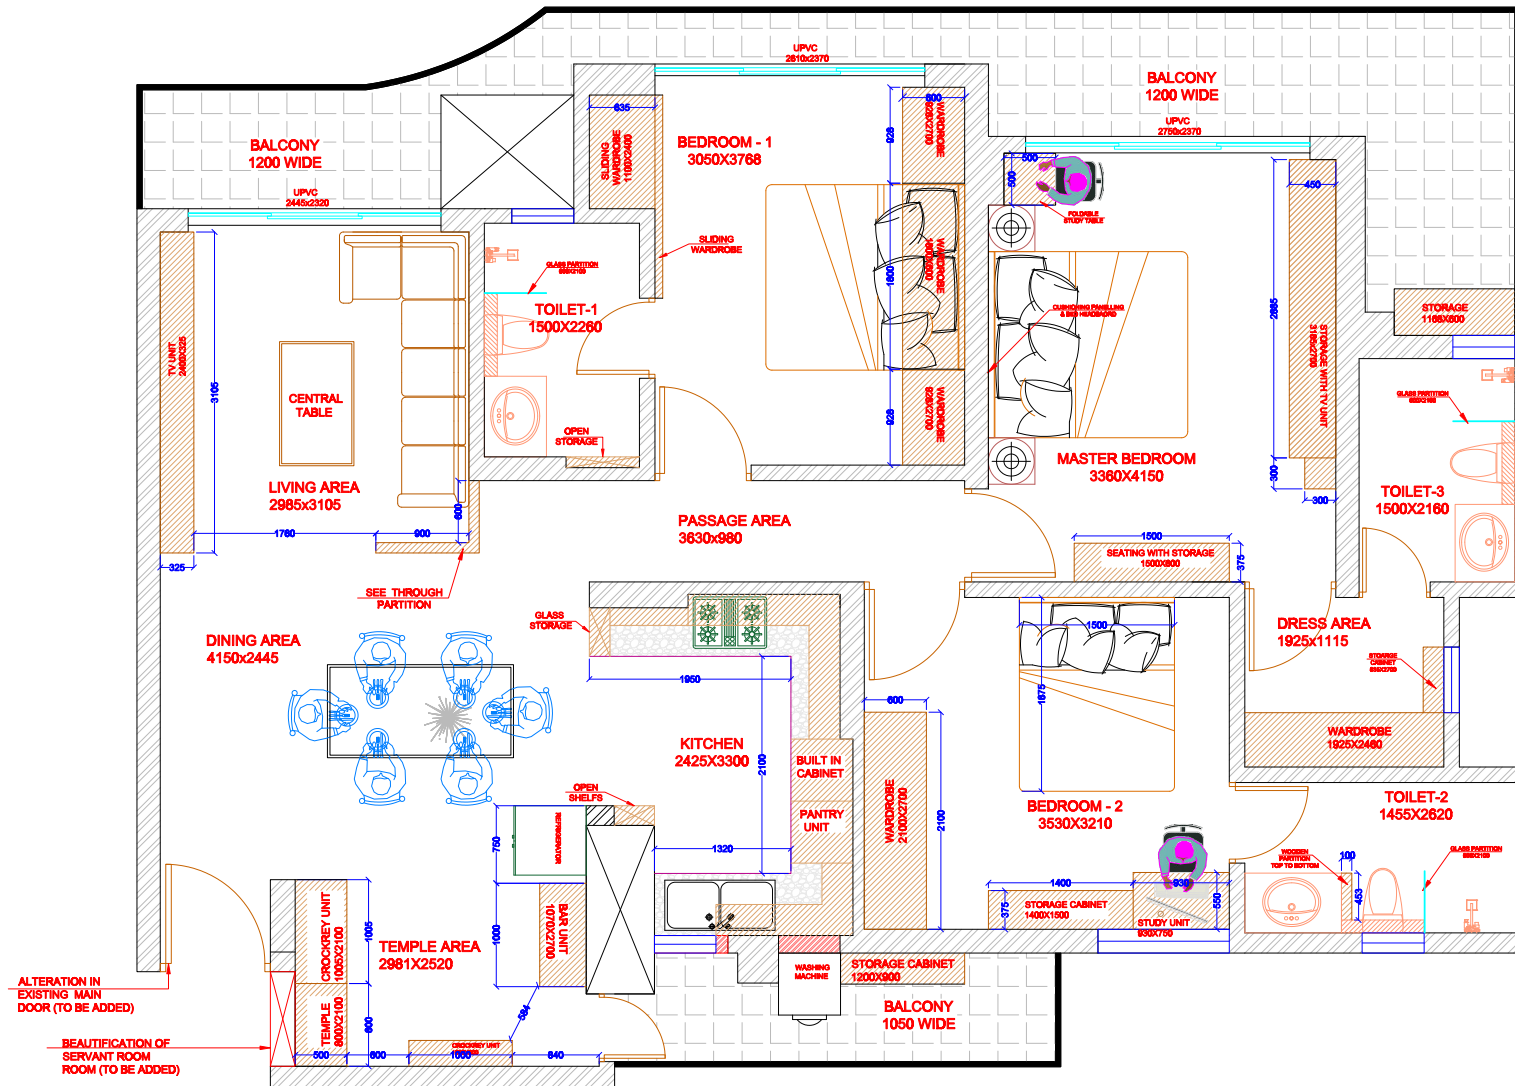

NOTE-

1. FLOOR TO CEILING HEIGHT=2855 MM
2. FLOOR TO BEAM HEIGHT=2480 MM
3. DOOR HEIGHT=2100 MM
4. MAIN DOOR HEIGHT=2410 MM
5. ALL DIMENSIONS ARE IN MM
6. DO ALL THE CONDUITING WORK OF AC BEFORE FALSE CEILING
7. STRIP LIGHT RFT IS INCLUDED 10% CONTINGENCY

HIGH CREATIONS INTERIORS PVT LTD.

SPACE PLANNING & INTERIORS

● www.hcinterior.in

⚡ H-101, BASEMENT SECTOR -63, NOIDA
-201301

✉ info@hcinteriors.in, hcinteriorsprojectspvt.ltd

HC
INTERIOR
PLANS DESIGN

TITLE :- FURNITURE LAYOUT

DESIGN BY :-
AASIM SAIFI

DATE :-
02-05-2023

SCALE :- NTS

REV. DATE :-
10-05-2023

01

CLIENT REMARK :-

MR.ANUJ

PROJECT/SITE :-

SEC -102 GURGAON